

GARAGE REPLACEMENT / DESIGN REVIEW

Proposed building / floor plan



FLOOR PLAN NOTES

Front is the vehicle entrance.

Left bay: paired doors.

Full partition is provisional.

Dashed outline = assumed roof extent.

Clear openings from assumed posts:

Bay 1: 2775 mm (provisional)

Bay 2: 2850 mm (provisional)

Bay 3: 2775 mm (provisional)

150 mm posts; 100 mm walls assumed.

Nominal bay divisions are not clear widths.


No foundations or structure specified.

Dark rainwater goods per S7; route TBC.

Preliminary - reference dimensions, subject to verification

A3 landscape | 1:50 at 100% print | Dimensions mm | Do not scale JPEG references


Site/address and compass orientation unconfirmed | 14 Sep 2026 | Revision P02

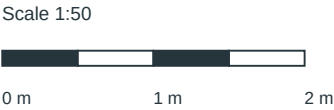

GARAGE REPLACEMENT / DESIGN REVIEW

Proposed building / front elevation

All heights relative to provisional ground datum 0.

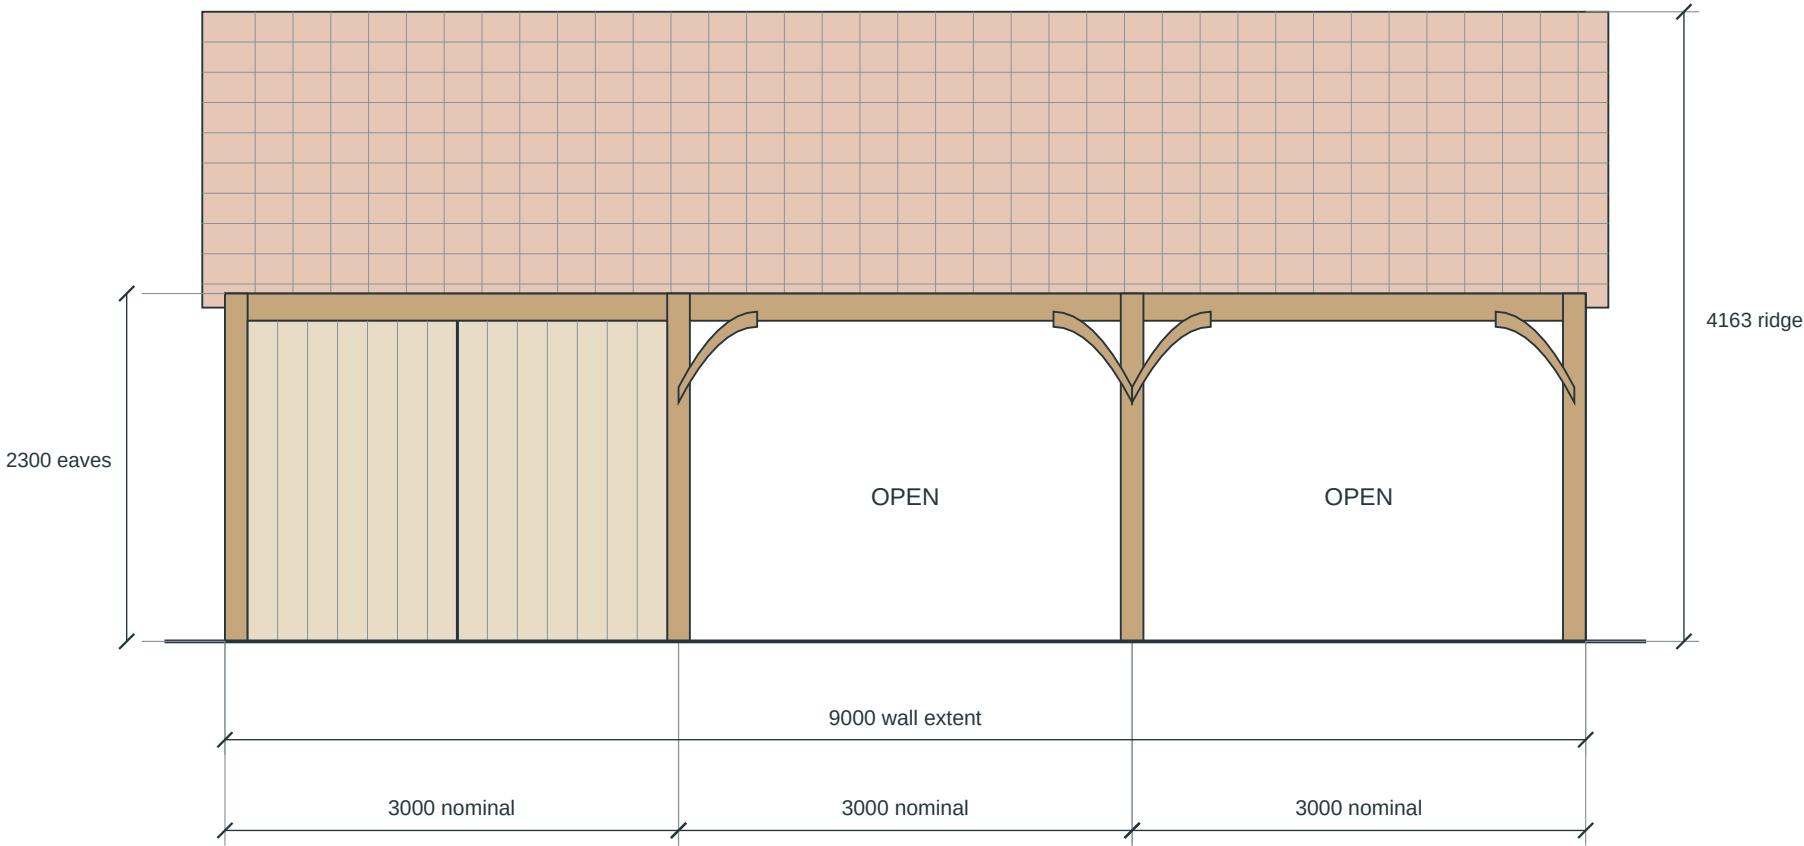


Roof: 31.84 deg derived from span and heights; source 30 deg conflicts.
Traditional oak frame / natural timber boarding / red profiled roof tiles (S6/S7).
Red brick plinth retained; frame sizes, joints and clay/concrete tile product unverified.

Preliminary - reference dimensions, subject to verification

A3 landscape | 1:50 at 100% print | Dimensions mm | Do not scale JPEG references


Site/address and compass orientation unconfirmed | 14 Sep 2026 | Revision P02

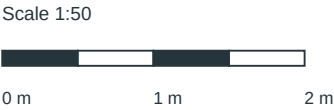

GARAGE REPLACEMENT / DESIGN REVIEW

Proposed building / rear elevation

All heights relative to provisional ground datum 0.

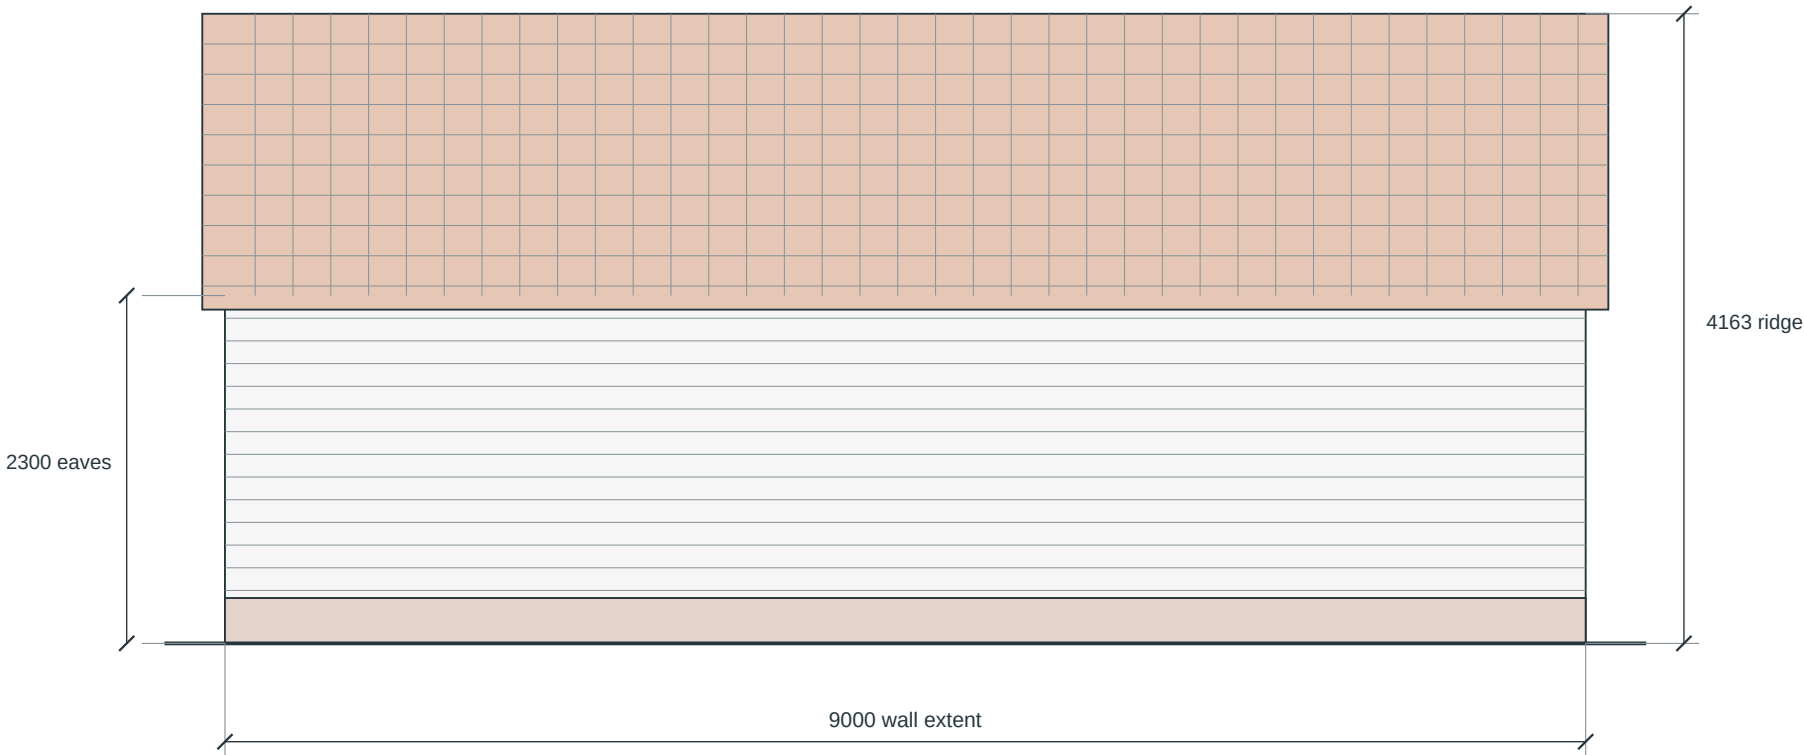


Roof: 31.84 deg derived from span and heights; source 30 deg conflicts.
Traditional oak frame / natural timber boarding / red profiled roof tiles (S6/S7).
Red brick plinth retained; frame sizes, joints and clay/concrete tile product unverified.

Preliminary - reference dimensions, subject to verification

A3 landscape | 1:50 at 100% print | Dimensions mm | Do not scale JPEG references


Site/address and compass orientation unconfirmed | 14 Sep 2026 | Revision P02

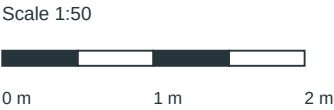

GARAGE REPLACEMENT / DESIGN REVIEW

Proposed building / left elevation

All heights relative to provisional ground datum 0.

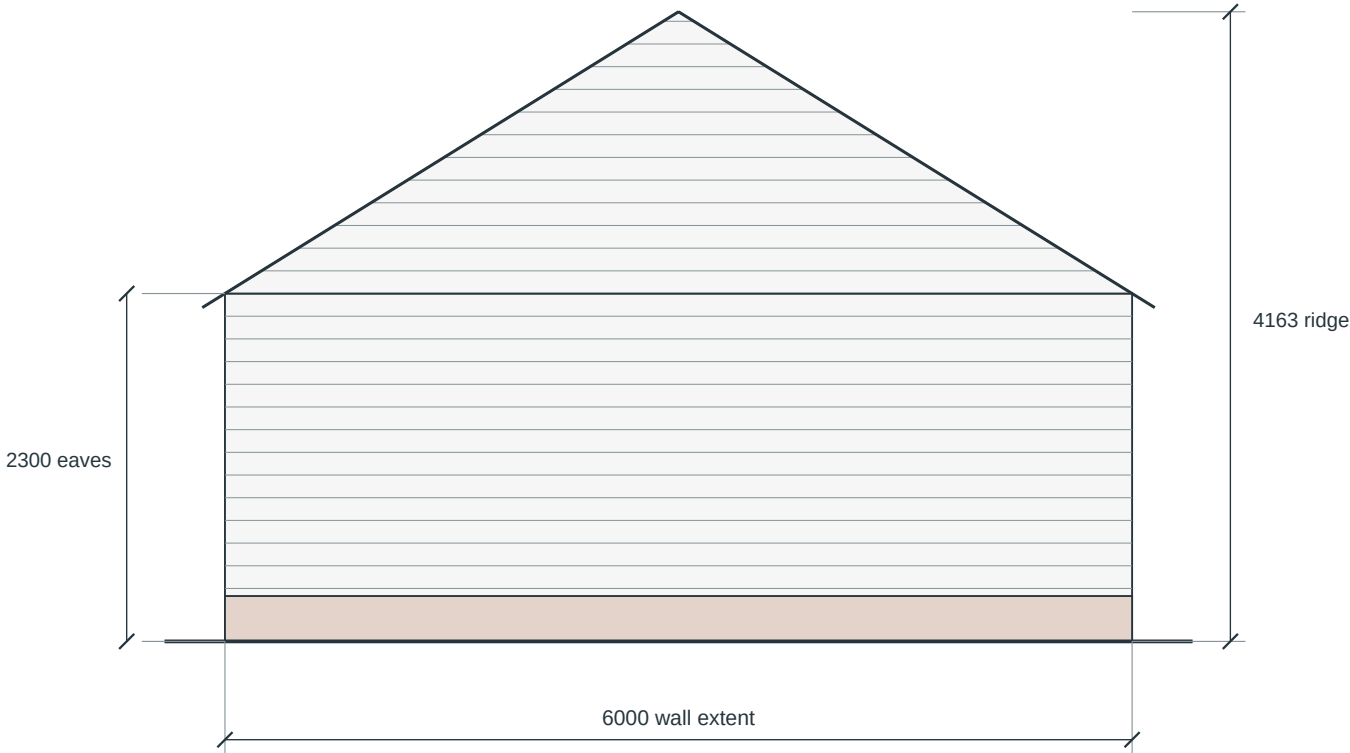

Roof: 31.84 deg derived from span and heights; source 30 deg conflicts.
Traditional oak frame / natural timber boarding / red profiled roof tiles (S6/S7).
Red brick plinth retained; frame sizes, joints and clay/concrete tile product unverified.

Preliminary - reference dimensions, subject to verification

A3 landscape | 1:50 at 100% print | Dimensions mm | Do not scale JPEG references


Site/address and compass orientation unconfirmed | 14 Sep 2026 | Revision P02



GARAGE REPLACEMENT / DESIGN REVIEW

Proposed building / right elevation

All heights relative to provisional ground datum 0.

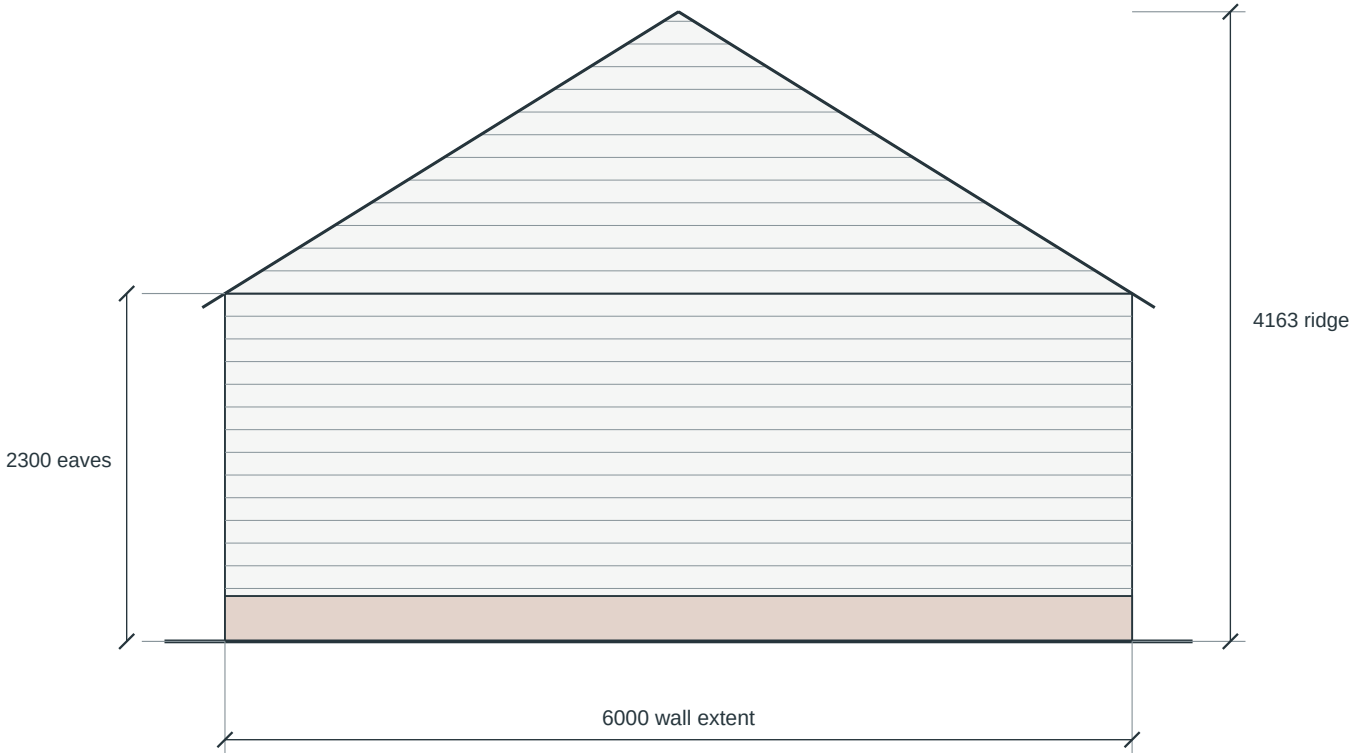


Roof: 31.84 deg derived from span and heights; source 30 deg conflicts.
Traditional oak frame / natural timber boarding / red profiled roof tiles (S6/S7).
Red brick plinth retained; frame sizes, joints and clay/concrete tile product unverified.

Preliminary - reference dimensions, subject to verification

A3 landscape | 1:50 at 100% print | Dimensions mm | Do not scale JPEG references


Site/address and compass orientation unconfirmed | 14 Sep 2026 | Revision P02

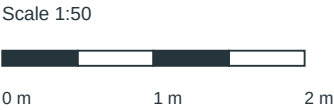

GARAGE REPLACEMENT / DESIGN REVIEW

Proposed building / schematic roof section

Geometric section | pitch 31.84 deg

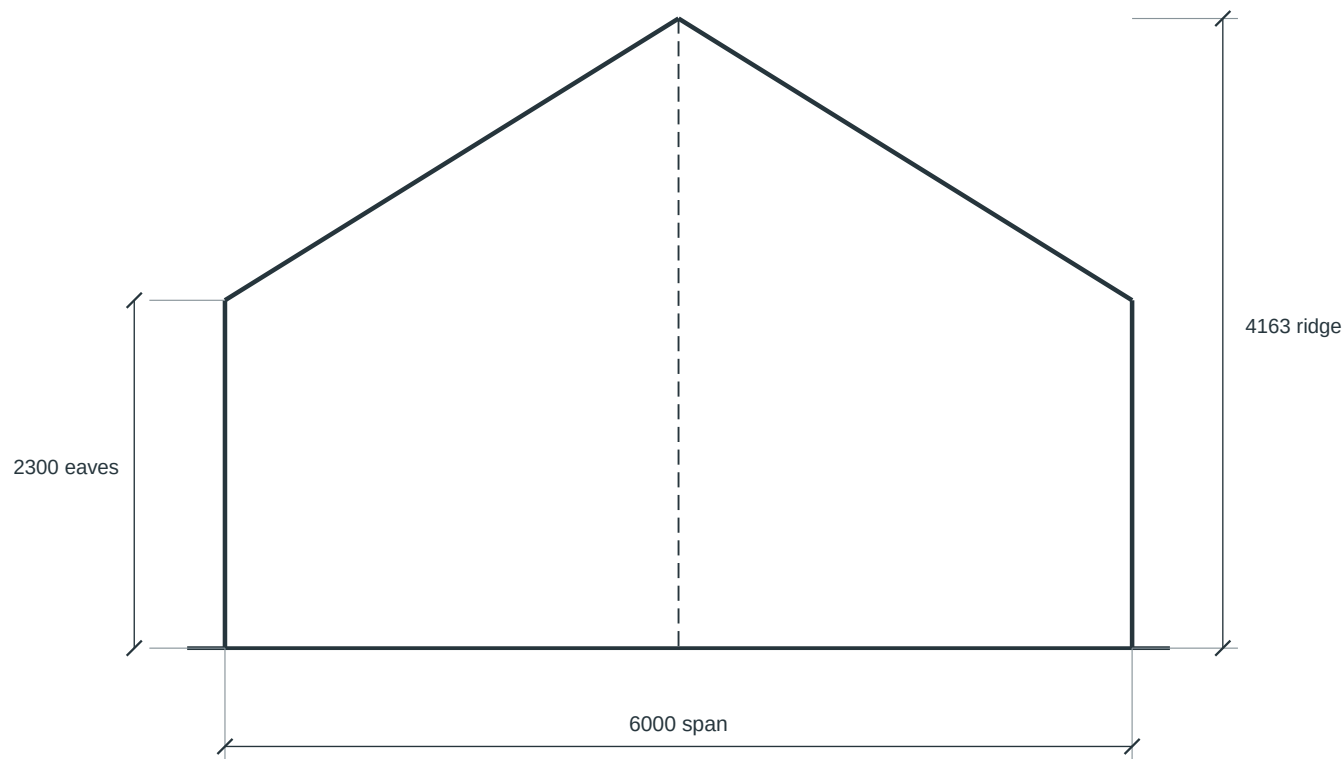

DATUM / GEOMETRY NOTES
Ground = provisional 0.
Eaves = roof surface at wall line.
Ridge = highest roof surface.
No roof build-up designed.
No foundations shown.

Section is geometric, not structural.
Verify heights and ground levels.

30 deg in the source would give a ridge of approximately 4032 mm.
P02 preserves 4163 mm and derives approximately 31.84 deg.
Source 3572 slope dimension has unresolved endpoints.
Pantile profile/ridge illustrated; 150 mm overhang and tile product unverified.

Preliminary - reference dimensions, subject to verification

A3 landscape | 1:50 at 100% print | Dimensions mm | Do not scale JPEG references

Site/address and compass orientation unconfirmed | 14 Sep 2026 | Revision P02

